

FIRE SPRINKLER SCOPE OF WORK NOTES:

1. FIRE SPRINKLER SCOPE OF WORK IS TO PROVIDE A COMPLETE, AUTOMATIC FIRE SPRINKLER SYSTEM FOR THE ENTIRE BUILDING IN ACCORDANCE WITH NFPA 13 AND APPLICABLE FACTORY MUTUAL DATA SHEETS.
2. PROVIDE MINIMUM 8-INCH FIRE PROTECTION SERVICE ENTRANCE. REFER TO CIVIL FOR CONTINUATION.
3. PROVIDE 5" STORZ FIRE DEPARTMENT CONNECTION.
4. PROVIDE CLASS I, MANUAL STANDPIPE SYSTEM FOR THE ENTIRE BUILDING IN ACCORDANCE WITH NFPA 14.
5. COORDINATE TEMPERATURE RATING OF SPRINKLERS NEAR HEAT PRODUCING SOURCES IN ACCORDANCE WITH NFPA 13 FOR ANTICIPATED AMBIENT CEILING TEMPERATURES.
6. DO NOT ROUTE SPRINKLER PIPING ABOVE ELECTRICAL DISTRIBUTION EQUIPMENT.
7. INSTALL SIDEWALL SPRINKLER WITHIN 2 FEET OF ELEVATOR HOISTWAY PIT FLOOR FOR HYDRAULIC ELEVATORS.
8. PROVIDE SPRINKLER PROTECTION AT THE TOP OF THE ELEVATOR HOISTWAY WHERE COMBUSTIBLES ARE PRESENT.
9. PROVIDE SPRINKLER PROTECTION AT THE TOP OF STAIRWAYS AND BENEATH THE LOWEST STAIRWAY LANDING.
10. PROVIDE SPRINKLER PROTECTION BELOW OPEN STAIR EXCEEDING 4' IN WIDTH. ROUTE PIPING TO MINIMIZE VISIBILITY. PAINT TO MATCH SURROUNDING FINISH. PROVIDE PROTECTIVE GUARD ON SPRINKLER.
11. PROVIDE SPRINKLER PROTECTION BELOW OVERHEAD DOORS AS REQUIRED PER NFPA 13. PIPING SHALL BE SUPPORTED FROM BUILDING STRUCTURE, NOT DOOR TRACKS.
12. PROVIDE LISTED, HEAVY-DUTY PROTECTIVE SPRINKLER GUARDS WHERE SPRINKLERS ARE INSTALLED BELOW 8 FEET OR IN LOCATIONS SUBJECT TO DAMAGE.
13. PROVIDE CORROSION RESISTENT SPRINKLERS IN AREAS SUBJECT TO HIGH HUMIDITY OR CORROSIVE ENVIRONMENTS.

FIRE ALARM SCOPE OF WORK NOTES:

1. FIRE ALARM SCOPE OF WORK IS TO PROVIDE A NEW EMERGENCY VOICE/ALARM COMMUNICATION FIRE ALARM SYSTEM FOR THE ENTIRE BUILDING IN ACCORDANCE WITH NFPA 72.
2. PROVIDE REMOTE POWER SUPPLY TO POWER VISIBLE NOTIFICATION APPLIANCES.
3. PROVIDE FIRE DEPARTMENT KEY BOX FOR FIRE DEPARTMENT ACCESS. PROVIDE EQUIPMENT AND CONNECTIONS NECESSARY TO MONITOR KEY BOX INTERNAL SUPERVISORY SWITCH(ES), AS REQUIRED.
4. PROVIDE LISTED FIRE ALARM GUARD OR WIRE COVER TO PROTECT DEVICE FROM PHYSICAL DAMAGE WITHIN THE GYM AND OTHER AREAS WHERE EQUIPMENT MAY BE SUBJECT TO DAMAGE.
5. WHERE APPLIANCES ARE LOCATED IN AREAS WITH HIGH HUMIDITY OR EXTREME TEMPERATURES PROVIDE FIRE ALARM EQUIPMENT SUITABLE FOR ENVIRONMENTAL CONDITIONS.
6. WHERE CEILING MOUNTED FIRE ALARM APPLIANCES ARE INSTALLED IN AREAS WITH HIGH STRUCTURE, MOUNT NOTIFICATION APPLIANCE TO BOTTOM OF JOIST OR AT 30 FT AFF, WHICHEVER IS LOWER, IN ACCORDANCE WITH NFPA 72 REQUIREMENTS.
7. PROVIDE EQUIPMENT AND CONNECTION(S) TO MONITOR DUST COLLECTION SYSTEM.
8. PROVIDE EQUIPMENT AND CONNECTION(S) REQUIRED FOR ELEVATOR RECALL AND/OR SHUTDOWN. REFER TO SEQUENCE OF OPERATION FOR ADDITIONAL INFORMATION.
9. PROVIDE HEAT DETECTOR(S) WITHIN 2 FEET OF ALL SPRINKLERS IN ELEVATOR HOISTWAYS AND EQUIPMENT ROOMS. REFER TO SEQUENCE OF OPERATION FOR ADDITIONAL INFORMATION.
10. PROVIDE DUCT MOUNTED SMOKE DETECTOR FOR FAN SHUTDOWN WHERE UNITS SUPPLY CAPACITY EXCEEDS 2,000 GPM. INSTALL DETECTOR PER MANUFACTURER'S RECOMMENDATIONS. INSTALL DETECTOR PER MANUFACTURER'S SPECIFICATIONS.
11. PROVIDE DUCT-MOUNTED SMOKE DETECTOR (OR AREA DETECTOR IF APPLICABLE) FOR FIRE/SMOKE DAMPER ACTIVATION. DETECTOR SHALL BE INSTALLED WITHIN 5 FEET OF DAMPER PER NFPA 72. THE DETECTOR SELECTED SHALL BE SUITABLE FOR THE AIRFLOW PRESENT IN THE DUCT.
12. PROVIDE LOW VOLTAGE WIRING FROM DUCT DETECTOR TO REMOTE TEST STATION. MOUNT AT 48" AFF OR IN CEILING, LABEL FOR EQUIPMENT SERVED.
13. PROVIDE SMOKE DETECTOR FOR FIRE DOOR ACTIVATION OR MAGNETIC DOOR HOLD RELEASE IN ACCORDANCE WITH NFPA 72.
14. PROVIDE APPROPRIATE EQUIPMENT AND CONNECTION(S) REQUIRED FOR FIRE DOOR ACTIVATION OR MAGNETIC DOOR HOLD RELEASE UPON ALARM SIGNAL.
15. PROVIDE EXTERIOR WATERFLOW ALARM. CENTER ABOVE FIRE DEPARTMENT CONNECTION. CONNECT TO FIRE ALARM SYSTEM.
16. CONNECT FIRE SPRINKLER MONITORING DEVICES TO FIRE ALARM SYSTEM. COORDINATE QUANTITY AND LOCATION OF DEVICES WITH FIRE PROTECTION SYSTEMS.
17. CONNECT VALVE TAMPER SUPERVISORY SWITCH FOR STANDPIPE CONTROL VALVE TO FIRE ALARM SYSTEM. COORDINATE QUANTITY AND LOCATION OF DEVICES WITH SPRINKLER SYSTEM.
18. PROVIDE EQUIPMENT AND CONNECTIONS TO MONITOR FIRE PUMP AND PRESSURE MAINTENANCE PUMP CONTROLLER SUPERVISORY OUTPUT SIGNALS PER NFPA 20.
19. WHERE EQUIPMENT IS SUBJECT TO HIGH OR LOW TEMPERATURES, HIGH HUMIDITY, OR CORROSIVE ENVIRONMENTS, PROVIDE FIRE ALARM EQUIPMENT SUITABLE FOR ENVIRONMENTAL CONDITIONS.
20. PROVIDE A DISTRIBUTED ANTENNA SYSTEM FOR EMERGENCY RESPONDER RADIO COVERAGE THROUGHOUT THE BUILDING IN ACCORDANCE WITH SECTION 510 OF THE INTERNATIONAL FIRE CODE.

FIRE PROTECTION GENERAL NOTES:

1. PRIOR TO SUBMITTING BID, VISIT THE JOB SITE AND BECOME FULLY ACQUAINTED WITH THE EXISTING CONDITIONS OF THE PROJECT. REVIEW THE GENERAL NOTES, SPECIFICATIONS AND OTHER DRAWINGS FOR ADDITIONAL REQUIREMENTS WHICH MAY NOT BE SPECIFICALLY CALLED OUT IN THIS PORTION OF THE CONSTRUCTION DOCUMENTS. NOTIFY ARCHITECT, ENGINEER AND/OR OWNER OF CONFLICTS OR DISCREPANCIES PRIOR TO SUBMISSION OF BID.
2. SYSTEM DESIGN, INSTALLATION AND MATERIALS SHALL BE IN ACCORDANCE WITH APPLICABLE NFPA STANDARDS. SYSTEM SHALL ALSO MEET ALL APPLICABLE BUILDING CODES, FIRE CODES AND THE REQUIREMENTS OF THE AUTHORITY HAVING JURISDICTION AND INSURANCE CARRIER. VERIFY REQUIREMENTS PRIOR TO BID SUBMITTAL.
3. INFORMATION ON CONTRACT DOCUMENTS IS GENERAL INFORMATION AND FOR BID PURPOSES ONLY. CONTRACTOR SHALL BE FULLY RESPONSIBLE FOR THE FINAL SYSTEM DESIGN AND LAYOUT OF ALL COMPONENTS, COORDINATION WITH ALL OTHER TRADES, AND SYSTEM CALCULATIONS REQUIRED FOR APPROVAL BY THE AUTHORITY HAVING JURISDICTION, ENGINEER, AND OWNER'S INSURER.
4. THE CONTRACTOR SHALL FOLLOW THE ENGINEER OF RECORD'S SYSTEM DESIGN AND LAYOUT OF ALL COMPONENTS EXCEPT WHERE MODIFICATION TO THE DESIGN IS NECESSARY. MODIFICATIONS SHALL BE REFLECTED IN THE CONTRACTOR'S SHOP DRAWINGS AND CALCULATIONS.
5. DEVIATIONS FROM ENGINEER'S DESIGN WILL NOT BE CONSIDERED UNLESS A FORMALLY SUBMITTED RFI IS RECEIVED AND APPROVED.
6. THE CONTRACTOR SHALL PROVIDE ALL EQUIPMENT AND LABOR REQUIRED FOR A COMPLETE AND OPERATIONAL SYSTEM AS INDICATED IN THE DRAWINGS AND SPECIFICATIONS.
7. PROVIDE ADDITIONAL MATERIALS AND LABOR REQUIRED DUE TO LACK OF COORDINATION OR TO MEET AUTHORITY HAVING JURISDICTION AND INSURANCE CARRIER REQUIREMENTS AT NO ADDITIONAL COST TO THE OWNER.
8. FORWARD COMPLETED CERTIFICATE OF COMPLETION AND CONTRACTOR MATERIAL TEST CERTIFICATES TO THE OWNER.
9. REFER TO SPECIFICATIONS FOR ADDITIONAL INFORMATION.

WATER SUPPLY INFORMATION:

OBTAINED FROM: CITY OF SALINA



TEST DATE: 04/07/2025  
TEST LOCATION: KSU TAC BUILDING  
STATIC PRESSURE: 72 PSI  
RESIDUAL PRESSURE: 35 PSI

FLOW HYDRANT 1 DESIGNATION: HYDRANT 1298  
NUMBER OF BUTTS FLOWED: 2  
HYDRANT COEFFICIENT: 0.90  
WATER FLOW: 1,318 GPM

FLOW HYDRANT 2 DESIGNATION: HYDRANT 1299  
NUMBER OF BUTTS FLOWED: 2  
HYDRANT COEFFICIENT: 0.90  
WATER FLOW: 995 GPM

TOTAL FLOW: 2,313 GPM

FIRE PROTECTION SYMBOLS
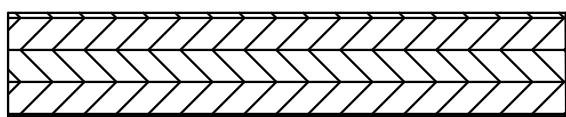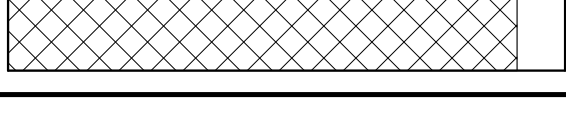
| THIS IS A MASTER LEGEND AND NOT ALL SYMBOLS OR ABBREVIATIONS ARE USED.                |                                                                                           |            |                              | V2.07   |  |  |  |
|---------------------------------------------------------------------------------------|-------------------------------------------------------------------------------------------|------------|------------------------------|---|--|--|--|
| ABBREVIATIONS                                                                         |                                                                                           | FIRE ALARM |                              |   |  |  |  |
| AFF                                                                                   | ABOVE FINISHED FLOOR                                                                      | NIC        | NOT IN CONTRACT              |  FIRE ALARM CONTROL PANEL/UNIT   |  |  |  |
| AFG                                                                                   | ABOVE FINISHED GRADE                                                                      | OC         | ON CENTER                    |  RECESSED FIRE ALARM CONTROL PANEL/UNIT   |  |  |  |
| CD                                                                                    | CANDLE                                                                                    | PV         | POST INDICATOR VALVE         |  FIRE ALARM ANNUNCIATOR PANEL   |  |  |  |
| DI                                                                                    | DUCTILE IRON                                                                              | PRV        | PRESSURE REDUCING VALVE      |  RECESSED FIRE ALARM ANNUNCIATOR PANEL   |  |  |  |
| ESFR                                                                                  | EARLY SUPPRESSION FAST RESPONSE                                                           | RD         | RETURN DUCT                  |  AMPLIFIER PANEL   |  |  |  |
| ETR                                                                                   | EXISTING TO REMAIN                                                                        | REV        | REVISION                     |  REMOTE POWER SUPPLY   |  |  |  |
| FHC                                                                                   | FIRE HOSE CABINET                                                                         | SD         | SUPPLY DUCT                  |  REMOTE TEST STATION WITH INDICATING LIGHT   |  |  |  |
| FP                                                                                    | FIRE PROTECTION                                                                           | SF         | SQUARE FEET                  |  REMOTE INDICATING LIGHT   |  |  |  |
| GC                                                                                    | CONTRACTOR                                                                                | SFFF       | SYNTHETIC FLOURINE-FREE FOAM |  PRESSURE SWITCH LOW/HIGH   |  |  |  |
| GPM                                                                                   | GALLONS PER MINUTE                                                                        | TYP        | TYPICAL                      |  WATERFLOW ALARM SWITCH   |  |  |  |
| JB/J-BOX                                                                              | JUNCTION BOX                                                                              | UNO        | UNLESS NOTES OTHERWISE       |  CONTROL VALVE TAMPER SWITCH   |  |  |  |
| MAX                                                                                   | MAXIMUM                                                                                   | V          | VOLT(S)                      |  MAGNETIC DOOR HOLD OPEN DEVICE   |  |  |  |
| MIN                                                                                   | MINIMUM                                                                                   | W          | WATTS                        |  CONTROL MODULE   |  |  |  |
| N/A                                                                                   | NOT APPLICABLE                                                                            | WP         | WEATHERPROOF                 |  MONITOR MODULE   |  |  |  |
| ANNOTATION                                                                            |                                                                                           |            |                              |  FIRE DEPARTMENT KEY BOX   |  |  |  |
|    | FIRE PROTECTION PLAN NOTE CALLOUT                                                         |            |                              |  PULL STATION   |  |  |  |
|    | CONNECTION POINT OF NEW WORK TO EXISTING                                                  |            |                              |  FIREFIGHTER'S PHONE JACK   |  |  |  |
|    | DETAIL REFERENCE UPPER NUMBER INDICATES DETAIL NUMBER LOWER NUMBER INDICATES SHEET NUMBER |            |                              |  HEAT DETECTOR (E INDICATES ELEVATOR RECALL)   |  |  |  |
|    | SECTION CUT DESIGNATION                                                                   |            |                              |  SMOKE DETECTOR (E INDICATES ELEVATOR RECALL)   |  |  |  |
|    | DEDICATED EQUIPMENT ACCESS TILE                                                           |            |                              |  FLAME DETECTOR (UV: ULTRAVIOLET; IR: INFRARED; UV/IR: COMBO)   |  |  |  |
|    | ACCESS PANEL                                                                              |            |                              |  PROJECTED BEAM SMOKE DETECTOR   |  |  |  |
| FIRE SPRINKLERS                                                                       |                                                                                           |            |                              |  DUCT MOUNTED SMOKE DETECTOR (SD=SUPPLY/RD=RETURN)   |  |  |  |
|    | UPRIGHT SPRINKLER                                                                         |            |                              |  CARBON MONOXIDE DETECTOR   |  |  |  |
|    | PENDENT SPRINKLER                                                                         |            |                              |  AREA OF REFUGE 2-WAY COMMUNICATION SYSTEM   |  |  |  |
|    | CONCEALED SPRINKLER                                                                       |            |                              |  WALL MOUNTED AUDIBLE NOTIFICATION APPLIANCE #W INDICATES WATTAGE (VOICE EVACUATION SYSTEMS ONLY)   |  |  |  |
|    | DRY PENDENT SPRINKLER                                                                     |            |                              |  WALL MOUNTED VISIBLE NOTIFICATION APPLIANCE #W INDICATES CANDELA   |  |  |  |
|    | DRY SIDEWALL SPRINKLER                                                                    |            |                              |  WALL MOUNTED AUDIBLE/VISIBLE NOTIFICATION APPLIANCE #W INDICATES CANDELA   |  |  |  |
|    | SIDEWALL SPRINKLER                                                                        |            |                              |  WALL MOUNTED AUDIBLE NOTIFICATION APPLIANCE #W INDICATES WATTAGE (VOICE EVACUATION SYSTEMS ONLY)   |  |  |  |
| FIRE SPRINKLER PIPING                                                                 |                                                                                           |            |                              |  CEILING MOUNTED AUDIBLE NOTIFICATION APPLIANCE #W INDICATES WATTAGE (VOICE EVACUATION SYSTEMS ONLY)   |  |  |  |
|    | FIRE PROTECTION (FP)                                                                      |            |                              |  CEILING MOUNTED VISIBLE NOTIFICATION APPLIANCE #W INDICATES CANDELA   |  |  |  |
|    | SHUTOFF VALVE                                                                             |            |                              |  CEILING MOUNTED AUDIBLE/VISIBLE NOTIFICATION APPLIANCE #W INDICATES CANDELA   |  |  |  |
|    | CHECK VALVE                                                                               |            |                              |  END OF LINE RESISTOR   |  |  |  |
|    | BACKFLOW PREVENTER                                                                        |            |                              |  ABORT SWITCH   |  |  |  |
|    | CAP                                                                                       |            |                              |  BELL   |  |  |  |
|    | ELBOW UP                                                                                  |            |                              | HATCHING LEGEND   |  |  |  |
|    | ELBOW DOWN                                                                                |            |                              |   |  |  |  |
|    | TEE UP                                                                                    |            |                              | LINETYPE LEGEND   |  |  |  |
|    | TEE DOWN                                                                                  |            |                              |   |  |  |  |
|    | FIRE DEPARTMENT CONNECTION                                                                |            |                              | THROUGHOUT THE DRAWINGS DIFFERENT LINETYPES ARE USED IN COMBINATION WITH THE SYMBOLS TO INDICATE THE STATUS OF ITEMS AS EXISTING, TO BE DEMOLISHED, TO BE INCLUDED AS PART OF NEW WORK AND/OR ITEMS WHICH ARE ANTICIPATED TO BE PROVIDED IN THE FUTURE. THE STATUS OF ITEMS USING THESE LINETYPES ARE RELATIVE TO THE VIEW IN WHICH THEY APPEAR. PHASING SHOWN IN DRAWINGS IS NOT INTENDED TO FULLY DESCRIBE ALL NECESSARY CONSTRUCTION PHASING, WHICH IS DETERMINED BY THE CONTRACTOR AS PART OF THEIR RESPONSIBILITIES. ANY SUCH PHASES DESCRIBED IN THE CONSTRUCTION DOCUMENTS ARE GENERAL AND ONLY INTENDED TO INDICATE A BROAD ORDER FOR THE SAKE OF DESCRIBING THE PROJECT. THE FOLLOWING LINETYPES MAY BE USED ON ANY DEVICE, EQUIPMENT, NOTE, LINE, SHAPE, ETC. |  |  |  |
|    | FIRE PUMP TEST HEADER                                                                     |            |                              |   |  |  |  |
|    | INSPECTOR'S TEST CONNECTION / AUXILIARY DRAIN                                             |            |                              | EXISTING _____ NEW _____   |  |  |  |
|    | SPRINKLER RISER                                                                           |            |                              |   |  |  |  |
|   | TOP BEAM CLAMP                                                                            |            |                              | DEMOLISH - - - - - FUTURE - - - - -   |  |  |  |
|  | TRAPEZE HANGER                                                                            |            |                              |   |  |  |  |
| STANDARD MOUNTING HEIGHTS                                                             |                                                                                           |            |                              | ENLARGED PLAN   |  |  |  |
| AUDIBLE APPLIANCE (TOP OF APPLIANCE)                                                  |                                                                                           |            |                              |   |  |  |  |
| FIRE ALARM ANNUNCIATOR PANEL (TOP OF DISPLAY)                                         |                                                                                           |            |                              | NOT IN SCOPE (NIS)   |  |  |  |
| FIRE ALARM BELL (EXTERIOR) (CENTERLINE)                                               |                                                                                           |            |                              |   |  |  |  |
| FIRE ALARM CONTROL PANEL/UNIT (TOP OF DISPLAY)                                        |                                                                                           |            |                              | SHEET LIST - FIRE PROTECTION   |  |  |  |
| PULL STATION (TOP OF DEVICE)                                                          |                                                                                           |            |                              |   |  |  |  |
| VISIBLE APPLIANCE (CENTERLINE)                                                        |                                                                                           |            |                              | SHEET NUMBER   |  |  |  |
|                                                                                       |                                                                                           |            |                              |   |  |  |  |
|                                                                                       |                                                                                           |            |                              | SHEET NAME   |  |  |  |
|                                                                                       |                                                                                           |            |                              |   |  |  |  |
| FP000                                                                                 | FIRE PROTECTION GENERAL NOTES AND LEGEND                                                  |            |                              |   |  |  |  |
| FP101.A                                                                               | FIRE PROTECTION PLAN - LEVEL 01 - AREA A                                                  |            |                              |   |  |  |  |
| FP101.B                                                                               | FIRE PROTECTION PLAN - LEVEL 01 - AREA B                                                  |            |                              |   |  |  |  |
| FP102.A                                                                               | FIRE PROTECTION PLAN - LEVEL 02 - AREA A                                                  |            |                              |   |  |  |  |
| FP102.B                                                                               | FIRE PROTECTION PLAN - LEVEL 02 - AREA B                                                  |            |                              |   |  |  |  |
| FP400                                                                                 | FIRE PROTECTION ENLARGED PLAN - FIRE RISER ROOM                                           |            |                              |   |  |  |  |
| FP500                                                                                 | FIRE PROTECTION DETAILS - FIRE ALARM                                                      |            |                              |   |  |  |  |
| FP501                                                                                 | FIRE PROTECTION DETAILS - FIRE SUPPRESSION                                                |            |                              |   |  |  |  |



HENDERSON  
ENGINEERS  
8846 ENCLAVE DRIVE, SUITE 300  
TOPEKA, KANSAS 66603  
TEL 913.742.5901 FAX 913.742.5901  
WWW.HENDERSONENGINEERS.COM  
K.S. EXPIRES 12/31/2025

DLR PROJECT NO:  
12-24111-00  
KSU PROJECT NO: 2025-035  
REVISIONS

Department of Administration  
Office of Facilities & Procurement  
Management Design, Construction &  
Engineering  
700 SW Harrison, Suite 1200  
Topeka, Kansas 66603  
Phone 785-296-8899

Owner  
KSU SALINA AEROSPACE EDUCATION HUB  
1829 Aerospace Drive  
SALINA, KANSAS 67401  
DATE: 10/22/25  
DRAWN BY: Author

FIRE PROTECTION  
GENERAL NOTES AND  
LEGEND  
A-015102  
FP000  
ORIGINAL CONSTRUCTION  
DOCUMENTS



Autodesk Docs\\12-24111-00\\KSU Salina Aerospace Education Hub\\240000079\\KSU Salina Aerospace - MEPF\_V24.rvt  
10/1/2025 11:17:33 AM

1 FIRE PROTECTION PLAN - LEVEL 01 - AREA A  
1/8" = 1'-0"

0 4' 8' 12'  
SCALE: 1/8"=1'-0"



#### FIRE PROTECTION PLAN NOTES:

- 1 SPRINKLER MAIN ROUTED TO DECK ABOVE. ROUTE TIGHT TO STRUCTURE AND TO MINIMIZE VISIBILITY. PAINT TO MATCH SURROUNDING FINISH.
- 2 PROVIDE NEW REMOTE FIRE ALARM ANNUNCIATOR PANEL WITH INTEGRAL MICROPHONE.
- 3 FIRE ALARM EQUIPMENT SHOWN OFFSET FOR CLARITY. CENTER ANNUNCIATOR PANEL ABOVE MANUAL PULL STATION. (CENTER FIRE ALARM APPLIANCE ABOVE MANUAL PULL STATION). (CENTER FIRE ALARM APPLIANCE ABOVE ANNUNCIATOR PANEL).
- 4 FIRE DEPARTMENT CONNECTION. REFER TO SPECIFICATIONS FOR ADDITIONAL INFORMATION.
- 5
- 6 PROVIDE SPRINKLER PROTECTION BELOW OVERHEAD DOOR AS REQUIRED PER NFPA 13. PIPING SHALL BE SUPPORTED FROM BUILDING STRUCTURE, NOT DOOR TRACKS.
- 7 PROVIDE EQUIPMENT AND CONNECTION(S) REQUIRED FOR ELEVATOR RECALL AND/OR SHUTDOWN. REFER TO SEQUENCE OF OPERATION FOR ADDITIONAL INFORMATION.
- 8 PROVIDE HEAT DETECTOR(S) WITHIN 2 FEET OF ALL SPRINKLERS IN AREA DESIGNATED. REFER TO SEQUENCE OF OPERATION FOR ADDITIONAL INFORMATION.
- 9 PROVIDE SMOKE DETECTOR FOR DOOR RELEASE IN ACCORDANCE WITH NFPA 72.
- 10 PROVIDE APPROPRIATE EQUIPMENT AND CONNECTION(S) REQUIRED TO RELEASE DOOR HOLDERS UPON ALARM SIGNAL FROM THE FIRE ALARM CONTROL PANEL.
- 11 PROVIDE SPRINKLER PROTECTION BELOW OPEN STAIR EXCEEDING 4' IN WIDTH. ROUTE PIPING TO MINIMIZE VISIBILITY. PAINT TO MATCH SURROUNDING FINISH. PROVIDE PROTECTIVE GUARD ON SPRINKLER.

#### FIRE ALARM

|      |   |
|------|---|
| FACP | FIRE ALARM CONTROL PANEL/UNIT   |
| FACP | RECESSED FIRE ALARM CONTROL PANEL/UNIT                                                                                                 |
| FADP | FIRE ALARM ANNUNCIATOR PANEL   |
| FADP | RECESSED FIRE ALARM ANNUNCIATOR PANEL                                                                                                  |
| AMP  | AMPLIFIER PANEL   |
| RPS  | REMOTE POWER SUPPLY   |
| RT   | REMOTE TEST STATION WITH INDICATING LIGHT                                                                                              |
| RL   | REMOTE INDICATING LIGHT   |
| PS   | PRESSURE SWITCH LOW/HIGH   |
| FS   | WATERFLOW ALARM SWITCH   |
| TV   | CONTROL VALVE TAMPER SWITCH   |
| OP   | MAGNETIC DOOR HOLD OPEN DEVICE   |
| CM   | CONTROL MODULE   |
| MM   | MONITOR MODULE   |
| DK   | FIRE DEPARTMENT KEY BOX   |
| PS   | PULL STATION   |
| PS   | FIREFIGHTER'S PHONE JACK   |
| ED   | HEAT DETECTOR (E INDICATES ELEVATOR RECALL)                                                                                            |
| ED   | SMOKE DETECTOR (E INDICATES ELEVATOR RECALL)                                                                                           |
| ED   | FLAME DETECTOR (UV: ULTRAVIOLET; IR: INFRARED; UV/IR: COMBO)                                                                           |
| ED   | PROJECTED BEAM SMOKE DETECTOR   |
| ED   | DUCT MOUNTED SMOKE DETECTOR (SD=SUPPLY/ROD=RETURN)                                                                                     |
| ED   | CARBON MONOXIDE DETECTOR   |
| ED   | AREA OF REFUGE 2-WAY COMMUNICATION SYSTEM                                                                                              |
| ED   | WALL MOUNTED AUDIBLE NOTIFICATION APPLIANCE<br>#W INDICATES WATTAGE (VOICE EVACUATION SYSTEMS ONLY)                                    |
| ED   | WALL MOUNTED VISIBLE NOTIFICATION APPLIANCE<br>#V INDICATES CANDELA                                                                    |
| ED   | WALL MOUNTED AUDIBLE/VISIBLE NOTIFICATION APPLIANCE<br>#W INDICATES WATTAGE (VOICE EVACUATION SYSTEMS ONLY)<br>#V INDICATES CANDELA    |
| ED   | CEILING MOUNTED AUDIBLE NOTIFICATION APPLIANCE<br>#W INDICATES WATTAGE (VOICE EVACUATION SYSTEMS ONLY)                                 |
| ED   | CEILING MOUNTED VISIBLE NOTIFICATION APPLIANCE<br>#V INDICATES CANDELA                                                                 |
| ED   | CEILING MOUNTED AUDIBLE/VISIBLE NOTIFICATION APPLIANCE<br>#W INDICATES WATTAGE (VOICE EVACUATION SYSTEMS ONLY)<br>#V INDICATES CANDELA |
| ED   | END OF LINE RESISTOR   |
| ED   | ABORT SWITCH   |
| ED   | BELL   |



Autodesk Docs\\12-2411-00 KSU Salina Aerospace Education Hub\\240000079 KSU Salina Aerospace - MEPF\_V04.rvt  
10/1/2025 11:17:45 AM



1 FIRE PROTECTION PLAN - LEVEL 01 - AREA B  
1/8" = 1'-0"

0 4' 8' 12'  
SCALE: 1/8"=1'-0"



- FIRE PROTECTION PLAN NOTES:**
1. PROVIDE NECESSARY EQUIPMENT TO CLOSE FIRE DOORS UPON ACTIVATION OF ADJACENT SMOKE DETECTOR OR WATERFLOW ALARM.
  2. PROVIDE DUCT MOUNTED SMOKE DETECTOR FOR FAN POWERED MECHANICAL AIR HANDLING EQUIPMENT SHUTDOWN. INSTALL DETECTOR PER MANUFACTURER'S RECOMMENDATIONS. REFER TO MECHANICAL SHEETS FOR EQUIPMENT AND DUCTWORK LAYOUT AND DETAILS.
  3. PROVIDE SMOKE DETECTOR FOR DOOR RELEASE IN ACCORDANCE WITH NFPA 72.
  4. PROVIDE SPRINKLER PROTECTION BELOW OVERHEAD DOOR AS REQUIRED PER NFPA 13. PIPING SHALL BE SUPPORTED FROM BUILDING STRUCTURE, NOT DOOR TRACKS.

| FIRE ALARM |   |
|------------|---|
|            | FIRE ALARM CONTROL PANEL/UNIT   |
|            | RECESSED FIRE ALARM CONTROL PANEL/UNIT                                                                                                 |
|            | FIRE ALARM ANNUNCIATOR PANEL   |
|            | RECESSED FIRE ALARM ANNUNCIATOR PANEL                                                                                                  |
|            | AMPLIFIER PANEL   |
|            | REMOTE POWER SUPPLY   |
|            | REMOTE TEST STATION WITH INDICATING LIGHT                                                                                              |
|            | REMOTE INDICATING LIGHT   |
|            | PRESSURE SWITCH LOW/HIGH   |
|            | WATERFLOW ALARM SWITCH   |
|            | CONTROL VALVE TAMPER SWITCH   |
|            | MAGNETIC DOOR HOLD OPEN DEVICE   |
|            | CONTROL MODULE   |
|            | MONITOR MODULE   |
|            | FIRE DEPARTMENT KEY BOX   |
|            | PULL STATION   |
|            | FIREFIGHTER'S PHONE JACK   |
|            | HEAT DETECTOR (E INDICATES ELEVATOR RECALL)                                                                                            |
|            | SMOKE DETECTOR (E INDICATES ELEVATOR RECALL)                                                                                           |
|            | FLAME DETECTOR (UV: ULTRAVIOLET; IR: INFRARED; UV/IR: COMBO)                                                                           |
|            | PROJECTED BEAM SMOKE DETECTOR   |
|            | DUCT MOUNTED SMOKE DETECTOR (SD=SUPPLY/RO=RETURN)                                                                                      |
|            | CARBON MONOXIDE DETECTOR   |
|            | AREA OF REFUGE 2-WAY COMMUNICATION SYSTEM                                                                                              |
|            | WALL MOUNTED AUDIBLE NOTIFICATION APPLIANCE<br>#W INDICATES WATTAGE (VOICE EVACUATION SYSTEMS ONLY)                                    |
|            | WALL MOUNTED VISIBLE NOTIFICATION APPLIANCE<br>## INDICATES CANDELA                                                                    |
|            | WALL MOUNTED AUDIBLE/VISIBLE NOTIFICATION APPLIANCE<br>## INDICATES CANDELA<br>#W INDICATES WATTAGE (VOICE EVACUATION SYSTEMS ONLY)    |
|            | CEILING MOUNTED AUDIBLE NOTIFICATION APPLIANCE<br>#W INDICATES WATTAGE (VOICE EVACUATION SYSTEMS ONLY)                                 |
|            | CEILING MOUNTED VISIBLE NOTIFICATION APPLIANCE<br>## INDICATES CANDELA                                                                 |
|            | CEILING MOUNTED AUDIBLE/VISIBLE NOTIFICATION APPLIANCE<br>## INDICATES CANDELA<br>#W INDICATES WATTAGE (VOICE EVACUATION SYSTEMS ONLY) |
|            | END OF LINE RESISTOR   |
|            | ABORT SWITCH   |
|            | BELL   |

© DLR Group

10/1/2025

**HENDERSON**  
ENGINEERS  
8345 ENCLAVE DRIVE, SUITE 300  
TEL 913.42.5000 FAX 913.42.5901  
WWW.HENDERSONENGINEERS.COM  
KS EXP. 0000078 E-305  
KS EXP. 0000078 E-305

DLR PROJECT NO:  
12-24111-00  
KSU PROJECT NO: 2025-035  
REVISIONS

Department of Administration  
Office of Facilities & Procurement  
Management Design, Construction &  
Operations  
700 SW Harrison, Suite 1200  
Topeka, Kansas 66603  
Phone 785-296-8899

Owner  
**KSU SALINA AEROSPACE EDUCATION HUB**  
1829 Aerospace Drive  
SALINA, KANSAS 67401

DRAWN BY: Author  
DATE: 10/20/25

FIRE PROTECTION PLAN -  
LEVEL 01 - AREA B


A-015102

FP101.B

ORIGINAL CONSTRUCTION  
DOCUMENTS




Autodesk Docs/12-24111-00 KSU Salina Aerospace Education Hub/240303079 KSU Salina Aerospace - MEPF V24.rvt  
10/1/2025 11:17:59 AM

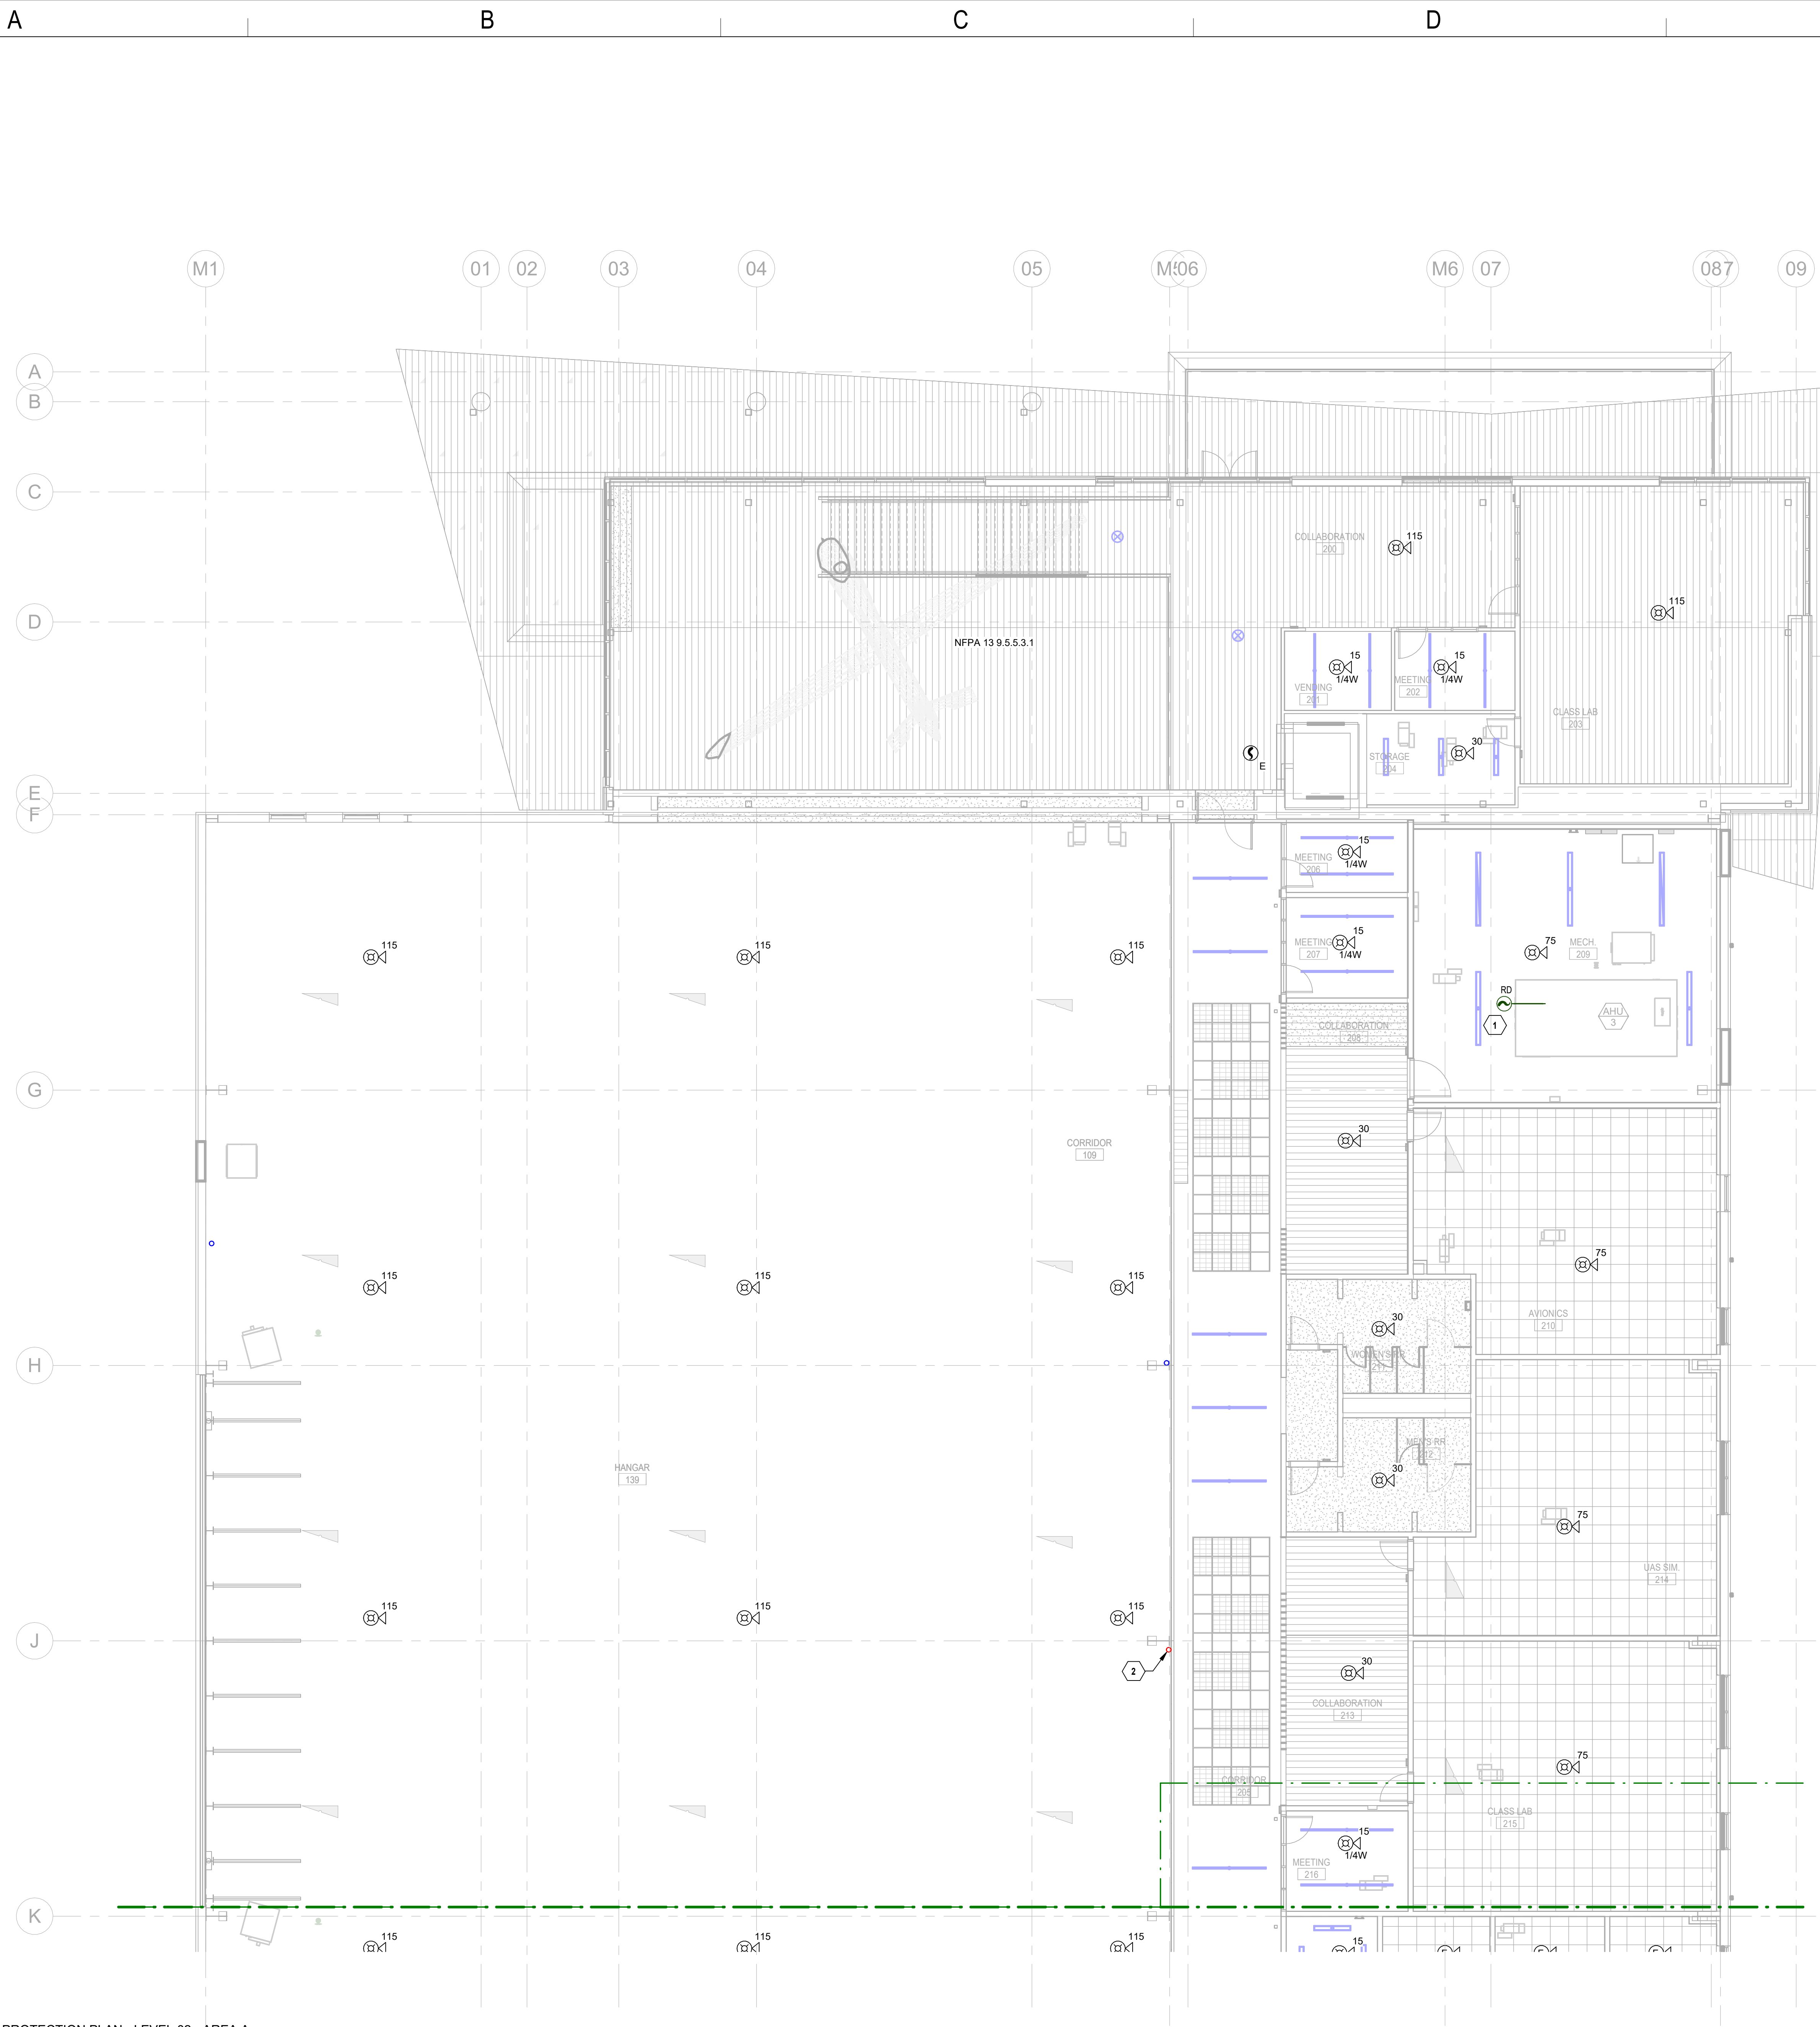

1 FIRE PROTECTION PLAN - LEVEL 02 - AREA A  
1/8" = 1'-0"

| FIRE ALARM |   |
|------------|---|
| [FACP]     | FIRE ALARM CONTROL PANEL/UNIT   |
| [FACP]     | RECESSED FIRE ALARM CONTROL PANEL/UNIT                                                                                                |
| [FAAP]     | FIRE ALARM ANNUNCIATOR PANEL   |
| [FAAP]     | RECESSED FIRE ALARM ANNUNCIATOR PANEL                                                                                                 |
| [AMP]      | AMPLIFIER PANEL   |
| [RPS]      | REMOTE POWER SUPPLY   |
| [RT]       | REMOTE TEST STATION WITH INDICATING LIGHT                                                                                             |
| [RL]       | REMOTE INDICATING LIGHT   |
| [PS]       | PRESSURE SWITCH LOW/HIGH   |
| [FS]       | WATERFLOW ALARM SWITCH   |
| [VT]       | CONTROL VALVE TAMPER SWITCH   |
| [DH]       | MAGNETIC DOOR HOLD OPEN DEVICE   |
| [CM]       | CONTROL MODULE   |
| [MM]       | MONITOR MODULE   |
| [K]        | FIRE DEPARTMENT KEY BOX   |
| [P]        | PULL STATION   |
| [F]        | FIREFIGHTER'S PHONE JACK   |
| [E]        | HEAT DETECTOR (E INDICATES ELEVATOR RECALL)                                                                                           |
| [V]        | SMOKE DETECTOR (E INDICATES ELEVATOR RECALL)                                                                                          |
| [V]        | FLAME DETECTOR (UV: ULTRAVIOLET; IR: INFRARED; UWIR: COMBO)                                                                           |
| [T]        | PROJECTED BEAM SMOKE DETECTOR   |
| [SD]       | DUCT MOUNTED SMOKE DETECTOR (SD=SUPPLY/RO=RETURN)                                                                                     |
| [CM]       | CARBON MONOXIDE DETECTOR   |
| [AR]       | AREA OF REFUGE 2-WAY COMMUNICATION SYSTEM                                                                                             |
| [EKA]      | WALL MOUNTED AUDIBLE NOTIFICATION APPLIANCE<br>#W INDICATES WATTAGE (VOICE EVACUATION SYSTEMS ONLY)                                   |
| [EVA]      | WALL MOUNTED VISIBLE NOTIFICATION APPLIANCE<br># INDICATES CANDELA                                                                    |
| [EKA#W]    | WALL MOUNTED AUDIBLE/VISIBLE NOTIFICATION APPLIANCE<br># INDICATES CANDELA<br>#W INDICATES WATTAGE (VOICE EVACUATION SYSTEMS ONLY)    |
| [EVA#W]    | CEILING MOUNTED AUDIBLE NOTIFICATION APPLIANCE<br>#W INDICATES WATTAGE (VOICE EVACUATION SYSTEMS ONLY)                                |
| [EVA#W]    | CEILING MOUNTED VISIBLE NOTIFICATION APPLIANCE<br># INDICATES CANDELA                                                                 |
| [EKA#W]    | CEILING MOUNTED AUDIBLE/VISIBLE NOTIFICATION APPLIANCE<br># INDICATES CANDELA<br>#W INDICATES WATTAGE (VOICE EVACUATION SYSTEMS ONLY) |
| [ELR]      | END OF LINE RESISTOR   |
| [AS]       | ABORT SWITCH   |
| [B]        | BELL   |

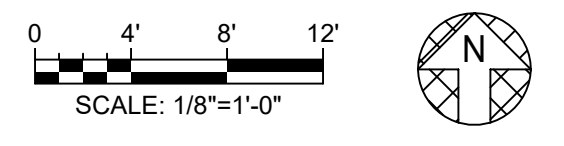

- FIRE PROTECTION PLAN NOTES:**
- 1 PROVIDE DUCT MOUNTED SMOKE DETECTOR FOR FAN POWERED MECHANICAL AIR HANDLING EQUIPMENT SHUTDOWN. INSTALL DETECTOR PER MANUFACTURER'S RECOMMENDATIONS. REFER TO MECHANICAL SHEETS FOR EQUIPMENT AND DUCTWORK LAYOUT AND DETAILS.
  - 2 SPRINKLER MAIN ROUTED TO DECK ABOVE. ROUTE TIGHT TO STRUCTURE AND TO MINIMIZE VISIBILITY. PAINT TO MATCH SURROUNDING FINISH.

© DLR Group

10/1/2025

**HENDERSON**  
ENGINEERS  
836 ENCLAVE DRIVE, SUITE 300  
TOPEKA, KANSAS 66603  
TEL 913.42.5000 FAX 913.42.5901  
WWW.HENDERSONENGINEERS.COM

250000079 E-SUS  
KS EXPIRES 12/31/2025

DLR PROJECT NO:  
12-24111-00

KSU PROJECT NO: 2025-035

REVISIONS

Department of Administration  
Office of Facilities & Procurement  
Management Design, Construction &  
Operations  
700 SW Harrison, Suite 1200  
Topeka, Kansas 66603  
Phone 785-296-8899

Owner  
**KSU SALINA AEROSPACE EDUCATION HUB**  
1829 Aerospace Drive  
SALINA, KANSAS 67401

DATE: 10/22/25

DRAWN BY: Author

FIRE PROTECTION PLAN -  
LEVEL 02 - AREA A


A-015102

FP102.A

ORIGINAL CONSTRUCTION  
DOCUMENTS



Autodesk Docs/12/24/11-00 KSU Salina Aerospace Education Hdb/240000079 KSU Salina Aerospace - MEPF 04.v4  
10/12/2025 11:18:07 AM

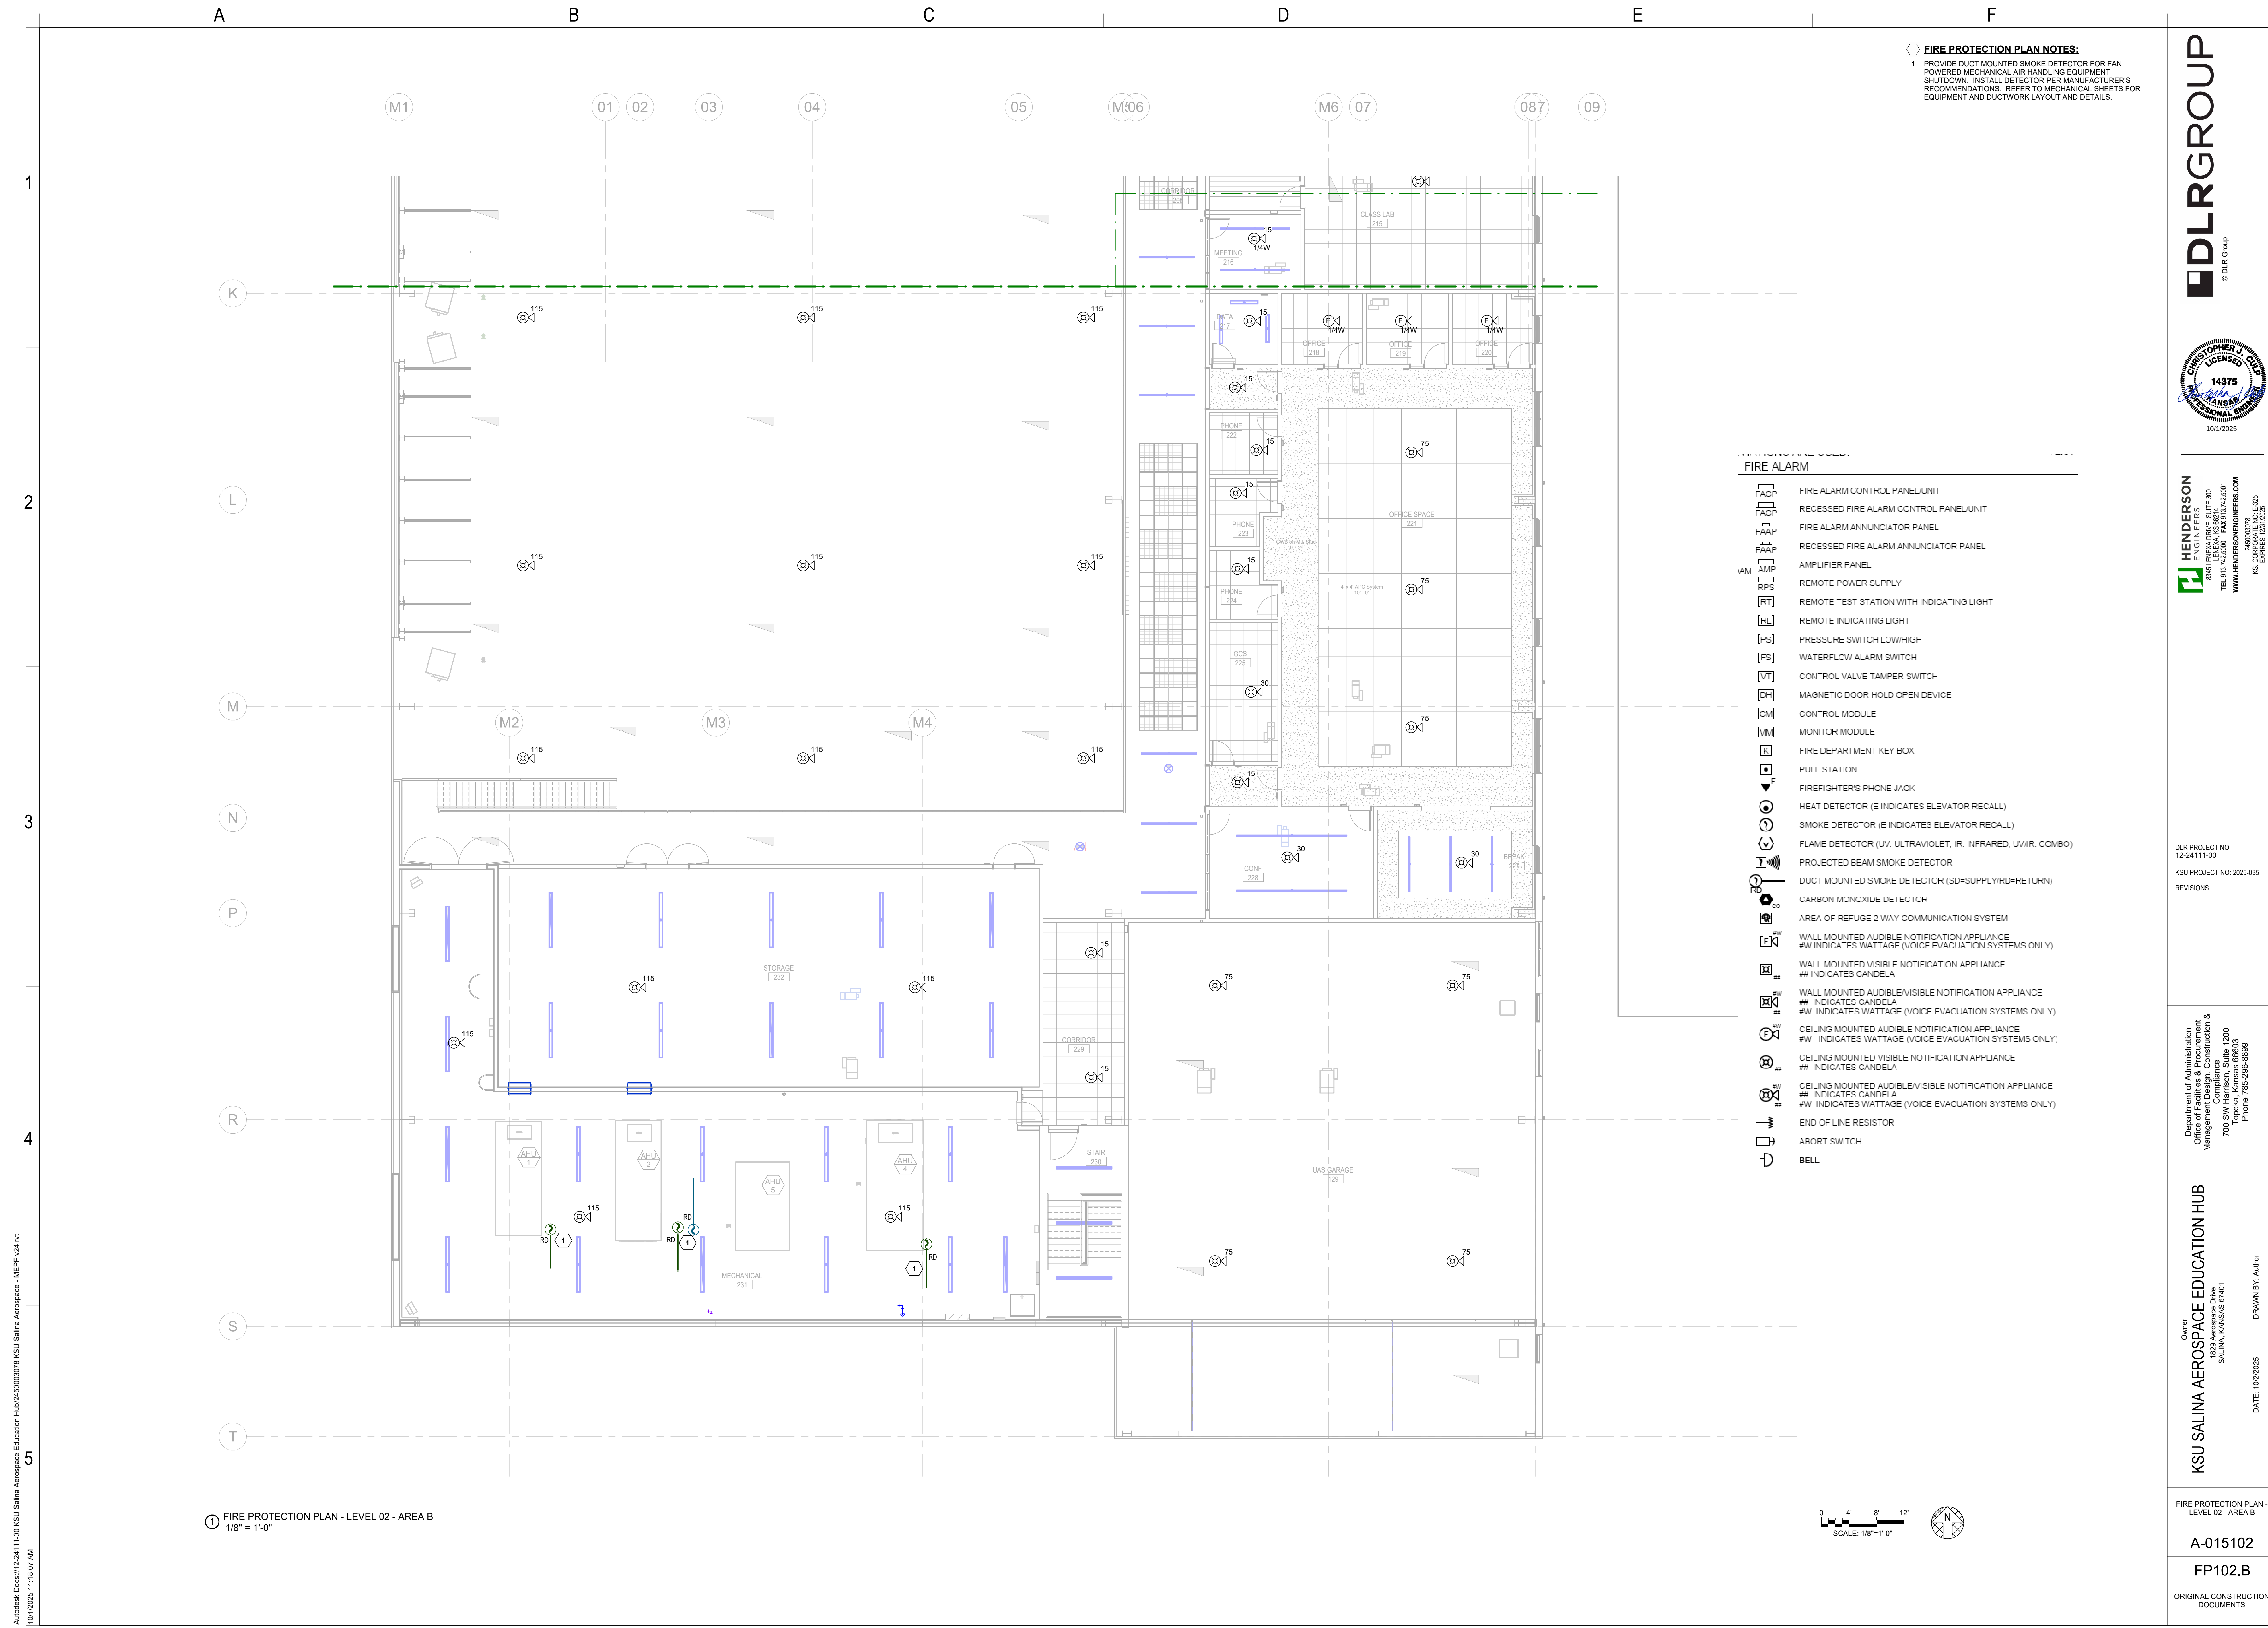

**FIRE PROTECTION PLAN NOTES:**  
1 PROVIDE DUCT MOUNTED SMOKE DETECTOR FOR FAN POWERED MECHANICAL AIR HANDLING EQUIPMENT SHUTDOWN. INSTALL DETECTOR PER MANUFACTURER'S RECOMMENDATIONS. REFER TO MECHANICAL SHEETS FOR EQUIPMENT AND DUCTWORK LAYOUT AND DETAILS.

- FIRE ALARM**
- [FACP] FIRE ALARM CONTROL PANEL/UNIT
  - [FACP] RECESSED FIRE ALARM CONTROL PANEL/UNIT
  - [FAAP] FIRE ALARM ANNUCIATOR PANEL
  - [FAAP] RECESSED FIRE ALARM ANNUCIATOR PANEL
  - [AMP] AMPLIFIER PANEL
  - [RPS] REMOTE POWER SUPPLY
  - [RT] REMOTE TEST STATION WITH INDICATING LIGHT
  - [RL] REMOTE INDICATING LIGHT
  - [PS] PRESSURE SWITCH LOW/HIGH
  - [FS] WATERFLOW ALARM SWITCH
  - [VT] CONTROL VALVE TAMPER SWITCH
  - [DH] MAGNETIC DOOR HOLD OPEN DEVICE
  - [CM] CONTROL MODULE
  - [MM] MONITOR MODULE
  - [K] FIRE DEPARTMENT KEY BOX
  - [PULL] PULL STATION
  - [FIRE] FIREFIGHTER'S PHONE JACK
  - [HEAT] HEAT DETECTOR (E INDICATES ELEVATOR RECALL)
  - [SMOKE] SMOKE DETECTOR (E INDICATES ELEVATOR RECALL)
  - [FLAME] FLAME DETECTOR (UV: ULTRAVIOLET; IR: INFRARED; UV/IR: COMBO)
  - [PBD] PROJECTED BEAM SMOKE DETECTOR
  - [SD] DUCT MOUNTED SMOKE DETECTOR (SD=SUPPLY/RD=RETURN)
  - [CMO] CARBON MONOXIDE DETECTOR
  - [AREA] AREA OF REFUGE 2-WAY COMMUNICATION SYSTEM
  - [WNA] WALL MOUNTED AUDIBLE NOTIFICATION APPLIANCE  
#W INDICATES WATTAGE (VOICE EVACUATION SYSTEMS ONLY)
  - [WNA] WALL MOUNTED AUDIBLE NOTIFICATION APPLIANCE  
# INDICATES CANDELA
  - [WNA] WALL MOUNTED AUDIBLE/VISIBLE NOTIFICATION APPLIANCE  
# INDICATES CANDELA  
#W INDICATES WATTAGE (VOICE EVACUATION SYSTEMS ONLY)
  - [CNA] CEILING MOUNTED AUDIBLE NOTIFICATION APPLIANCE  
#W INDICATES WATTAGE (VOICE EVACUATION SYSTEMS ONLY)
  - [CNA] CEILING MOUNTED VISIBLE NOTIFICATION APPLIANCE  
# INDICATES CANDELA
  - [CNA] CEILING MOUNTED AUDIBLE/VISIBLE NOTIFICATION APPLIANCE  
# INDICATES CANDELA  
#W INDICATES WATTAGE (VOICE EVACUATION SYSTEMS ONLY)
  - [ELR] END OF LINE RESISTOR
  - [AS] ABORT SWITCH
  - [BELL] BELL

© DLR Group

**HENDERSON**  
ENGINEERS  
836 ENCLAVE DRIVE, SUITE 300  
TOPEKA, KANSAS 66603  
TEL 913.42.5000 FAX 913.42.5901  
WWW.HENDERSONENGINEERS.COM

KSU PROJECT NO: 2025-035  
REVISIONS

Owner  
**KSU SALINA AEROSPACE EDUCATION HUB**  
1829 Aerospace Drive  
SALINA, KANSAS 67401

Department of Administration  
Office of Facilities & Procurement  
Management Design, Construction &  
Operations  
700 SW Harrison, Suite 1200  
Topeka, Kansas 66603  
Phone 785-296-8899

DATE: 10/22/25  
DRAWN BY: Author


FIRE PROTECTION PLAN -  
LEVEL 02 - AREA B

A-015102

FP102.B

ORIGINAL CONSTRUCTION  
DOCUMENTS

1 FIRE PROTECTION PLAN - LEVEL 02 - AREA B  
1/8" = 1'-0"

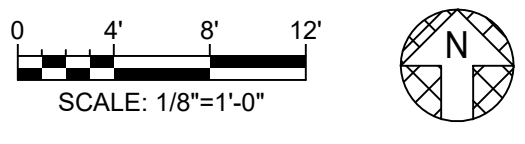



FIRE PROTECTION  
ENLARGED PLAN - FIRE  
RISER ROOM

---

A-015102

---

FP400

---

ORIGINAL CONSTRUCTION  
DOCUMENTS




Autodesk Docs\\12-24111-00 KSU Salina Aerospace Education Hub\\245000079 KSU Salina Aerospace - MEPF V4.rvt  
10/12/2025 11:18:22 AM

| SYSTEM INPUTS                                                             | PRIORITY |                     |                                    |                             |                             |                                                                   |                                                                   |                                                                   |                                                                   |                                                                   | SYSTEM OUTPUTS                            |                                             |                                             |                                             |                                             |                                             |                                             |                                             |                                             |                                             |
|---------------------------------------------------------------------------|----------|---------------------|------------------------------------|-----------------------------|-----------------------------|-------------------------------------------------------------------|-------------------------------------------------------------------|-------------------------------------------------------------------|-------------------------------------------------------------------|-------------------------------------------------------------------|-------------------------------------------|---------------------------------------------|---------------------------------------------|---------------------------------------------|---------------------------------------------|---------------------------------------------|---------------------------------------------|---------------------------------------------|---------------------------------------------|---------------------------------------------|
|                                                                           | ALARM    | SUPERVISORY TROUBLE | REPORT TO FIRE ALARM CONTROL PANEL | ACTIVATE GENERAL FIRE ALARM | ACTIVATE GENERAL FIRE ALARM | SHUTDOWN ASSOCIATED FAN POWERED MECHANICAL AIR HANDLING EQUIPMENT | SHUTDOWN ASSOCIATED FAN POWERED MECHANICAL AIR HANDLING EQUIPMENT | SHUTDOWN ASSOCIATED FAN POWERED MECHANICAL AIR HANDLING EQUIPMENT | SHUTDOWN ASSOCIATED FAN POWERED MECHANICAL AIR HANDLING EQUIPMENT | SHUTDOWN ASSOCIATED FAN POWERED MECHANICAL AIR HANDLING EQUIPMENT | INITIATE ELEVATOR RECALL TO PRIMARY FLOOR | INITIATE ELEVATOR RECALL TO ALTERNATE FLOOR | INITIATE ELEVATOR RECALL TO ALTERNATE FLOOR | INITIATE ELEVATOR RECALL TO ALTERNATE FLOOR | INITIATE ELEVATOR RECALL TO ALTERNATE FLOOR | INITIATE ELEVATOR RECALL TO ALTERNATE FLOOR | INITIATE ELEVATOR RECALL TO ALTERNATE FLOOR | INITIATE ELEVATOR RECALL TO ALTERNATE FLOOR | INITIATE ELEVATOR RECALL TO ALTERNATE FLOOR | INITIATE ELEVATOR RECALL TO ALTERNATE FLOOR |
| SIGNALING LINE OR NOTIFICATION APPLIANCE CIRCUIT - OPEN                   |          |                     
| SIGNALING LINE OR NOTIFICATION APPLIANCE CIRCUIT - SHORT                  |          |                     
| SIGNALING LINE OR NOTIFICATION APPLIANCE CIRCUIT - GROUND                 |          |                     
| FIRE ALARM CONTROL PANEL LOSS OF POWER                                    |          |                     
| MANUAL PULL STATION                                                       |          |                     
| SMOKE DETECTOR - SPOT TYPE                                                |          |                     
| SMOKE DETECTOR - DUCT MOUNTED                                             |          |                     
| HEAT DETECTOR - SPOT TYPE                                                 |          |                     
| WATERFLOW ALARM SWITCH                                                    |          |                     
| VALVE TAMPER SWITCH                                                       |          |                     
| FIRE DEPARTMENT KEY BOX TAMPER SWITCH (KNOX BOX)                          |          |                     
| SMOKE DETECTOR - ELEVATOR LOBBY - PRIMARY FLOOR                           |          |                     
| SMOKE DETECTOR - ELEVATOR LOBBY - ALTERNATE FLOOR(S)                      |          |                     
| SMOKE DETECTOR - ELEVATOR EQUIPMENT ROOM                                  |          |                     
| HEAT DETECTOR - ELEVATOR EQUIPMENT ROOM / ABOVE LOWEST LEVEL OF DISCHARGE |          |                     

CONTRACTOR TO PROVIDE ALL NECESSARY EQUIPMENT AND CONNECTIONS REQUIRED TO ACCOMPLISH THE FUNCTIONS INDICATED, AT MINIMUM.

SEQUENCE OF OPERATIONS INDICATED IS SCHEMATIC. MODIFY TO SUIT CONDITIONS AND MEET APPLICABLE CODE REQUIREMENTS.

② FIRE ALARM SEQUENCE OF OPERATIONS  
NTS

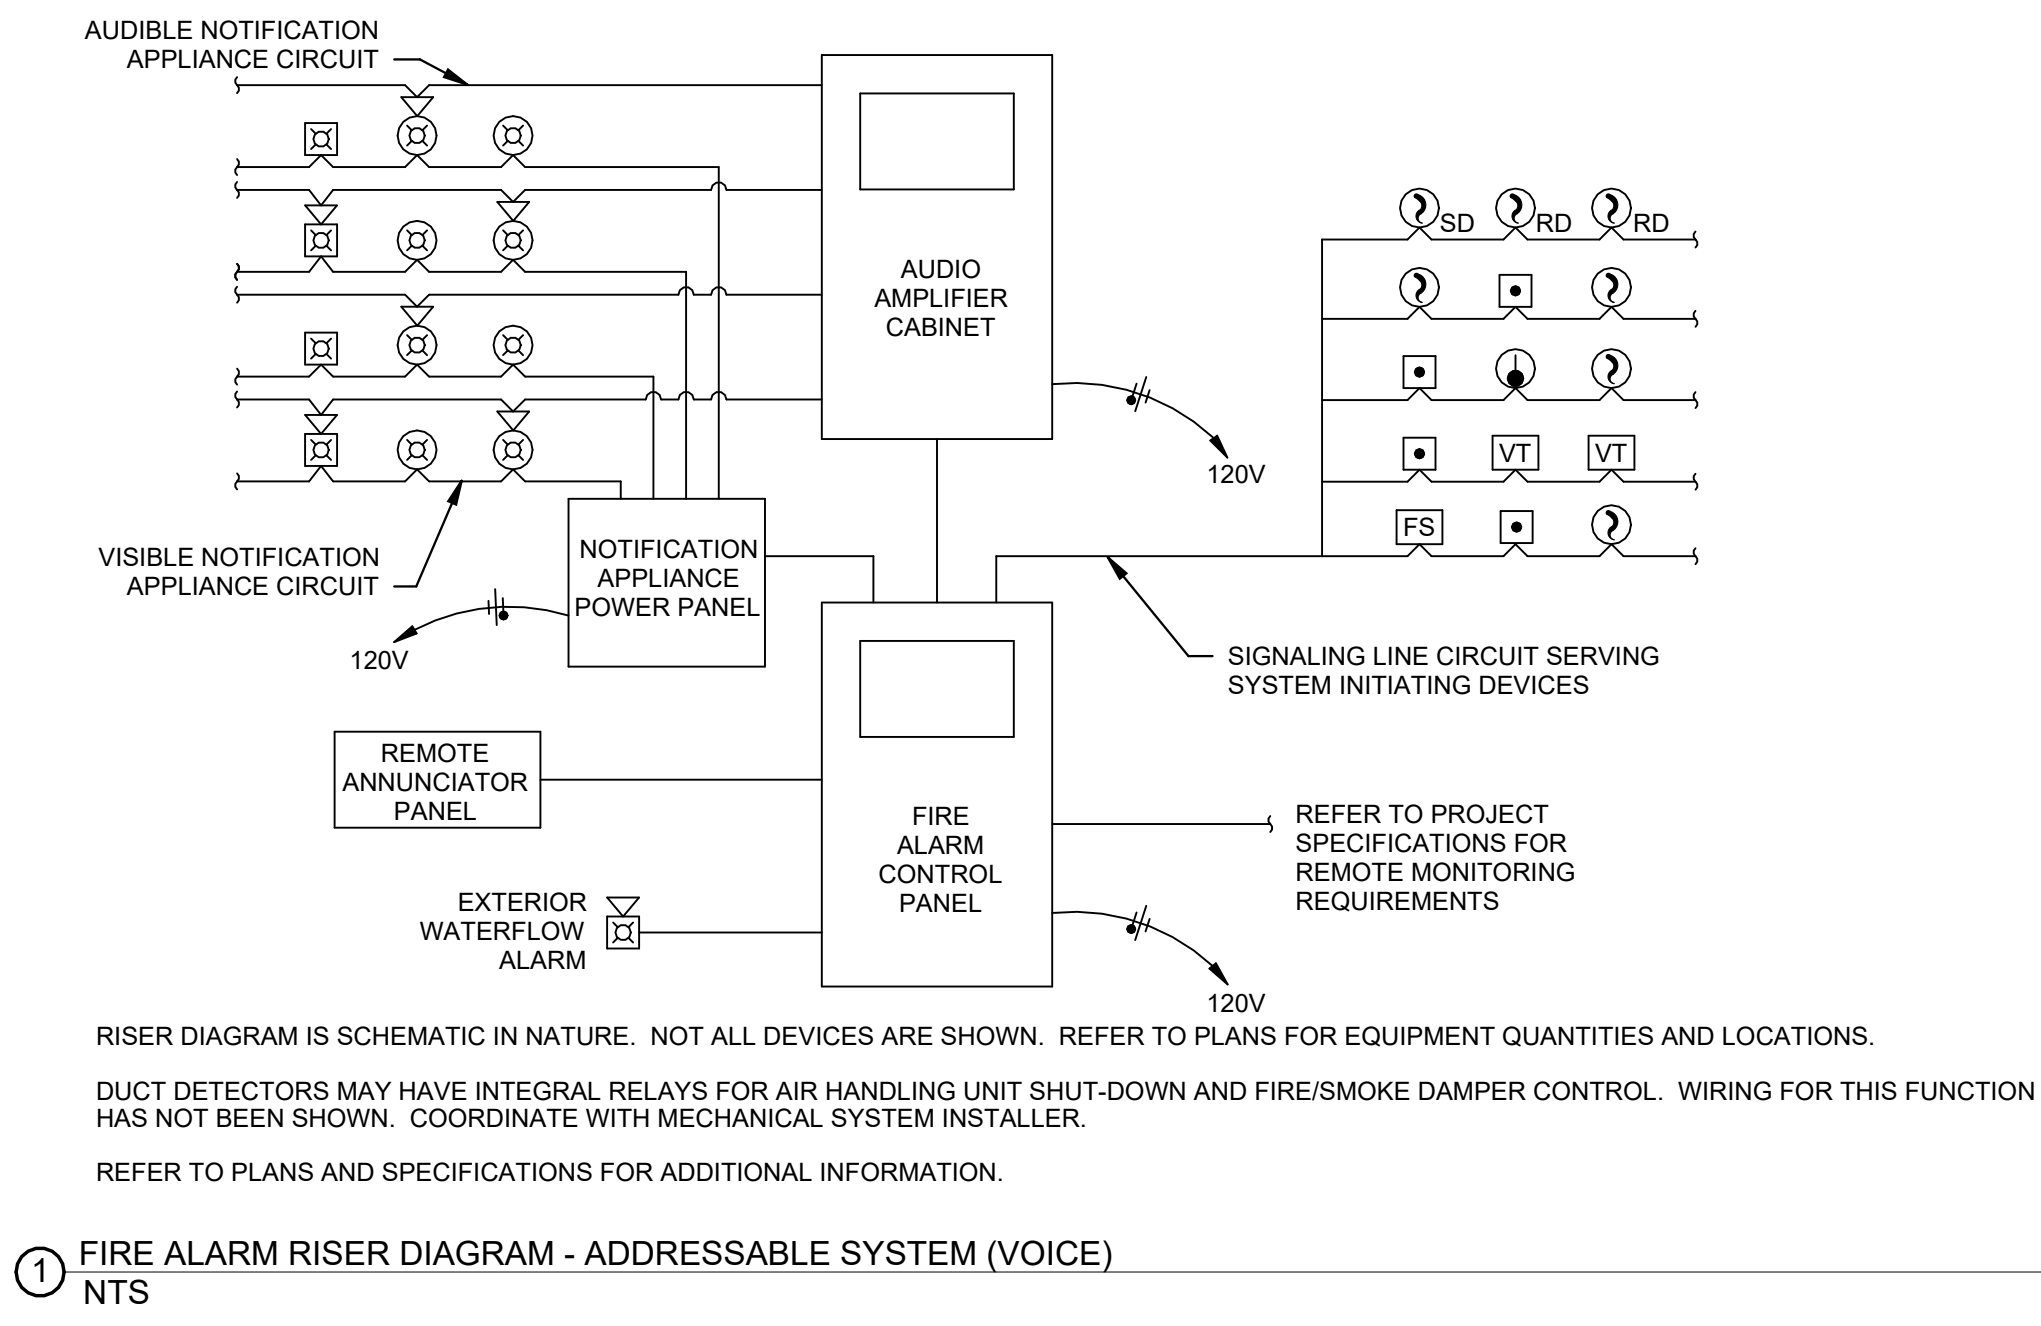

**HENDERSON**  
ENGINEERS  
8345 ENCLAVE DRIVE, SUITE 300  
TOPEKA, KANSAS 66603  
TEL 785.296.8899 FAX 785.296.8899  
WWW.HENDERSONENGINEERS.COM  
KS. EXPIRES 12/31/2025

DLR PROJECT NO:  
12-24111-00  
KSU PROJECT NO: 2025-035  
REVISIONS

Department of Administration  
Office of Facilities & Procurement  
Management Design, Construction &  
700 SW Harrison, Suite 1200  
Topeka, Kansas 66603  
Phone 785-296-8899

Owner  
**KSU SALINA AEROSPACE EDUCATION HUB**  
1829 Aerospace Drive  
SALINA, KANSAS 67401  
DATE: 10/22/25  
DRAWN BY: Author

FIRE PROTECTION DETAILS  
- FIRE ALARM  
A-015102  
FP500  
ORIGINAL CONSTRUCTION DOCUMENTS